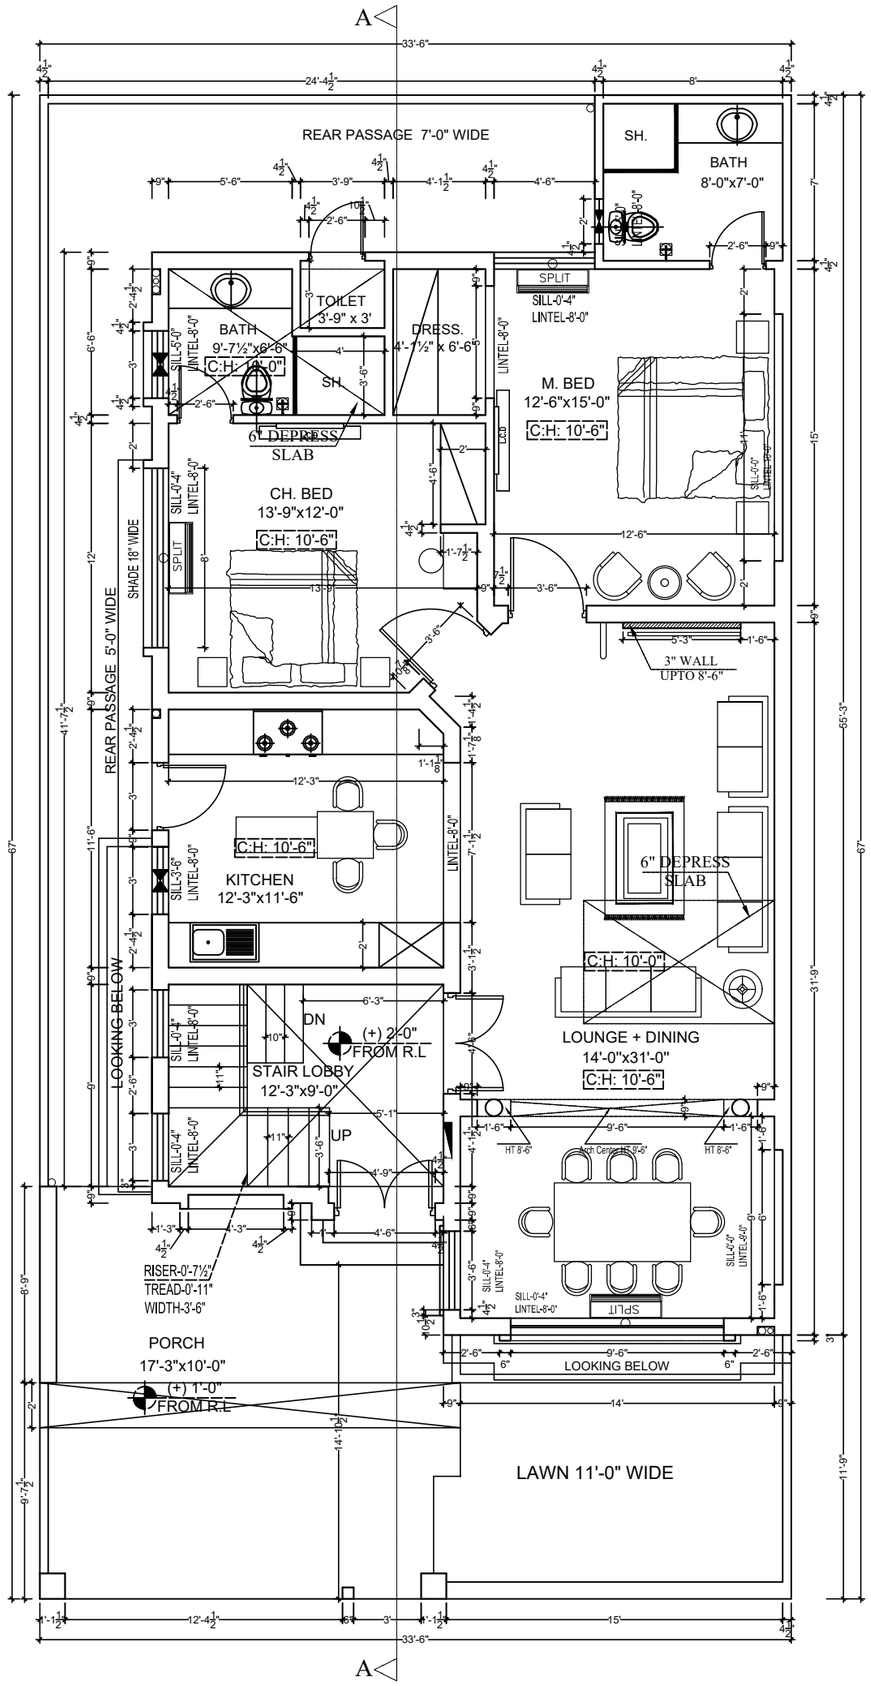
A
33'-6"
REAR PASSAGE 7'-0" WIDE
SH.
BATH
8'-0"x7'-0"
SPLIT
SILL-0'-4"
LINTEL-8'-0"
TOILET
3'-9" x 3'
BATH
9'-7½"x6'-6"
C.H: 10'-0"
SH
DRESS.
4'-7½" x 6'-6"
6" DEPRESS
SLAB
M. BED
12'-6"x15'-0"
C.H: 10'-6"
CH. BED
13'-9"x12'-0"
C.H: 10'-6"
SHADE 18" WIDE
REAR PASSAGE 5'-0" WIDE
3" WALL
UPTO 8'-6"
KITCHEN
12'-3"x11'-6"
C.H: 10'-6"
6" DEPRESS
SLAB
C.H: 10'-0"
LOOKING BELOW
DN
(+) 2'-0"
FROM R.L
STAIR LOBBY
12'-3"x9'-0"
UP
LOUNGE + DINING
14'-0"x31'-0"
C.H: 10'-6"
HT 8'-6"
RISER-0'-7½"
TREAD-0'-11"
WIDTH-3'-6"
PORCH
17'-3"x10'-0"
(+) 1'-0"
FROM R.L
LOOKING BELOW
LAWN 11'-0" WIDE
A